


Identificativi Catastali: Sezione: Foglio: 9 Particella: 663 Subalterno: 12	Compilata da: Iscritto all'albo: Prov. _____ N. _____
---	---

Scheda n. 1 Scala 1:100

Ufficio
Secondo piano
Interno 6
H = 3,00 m
Soluzione A - progetto

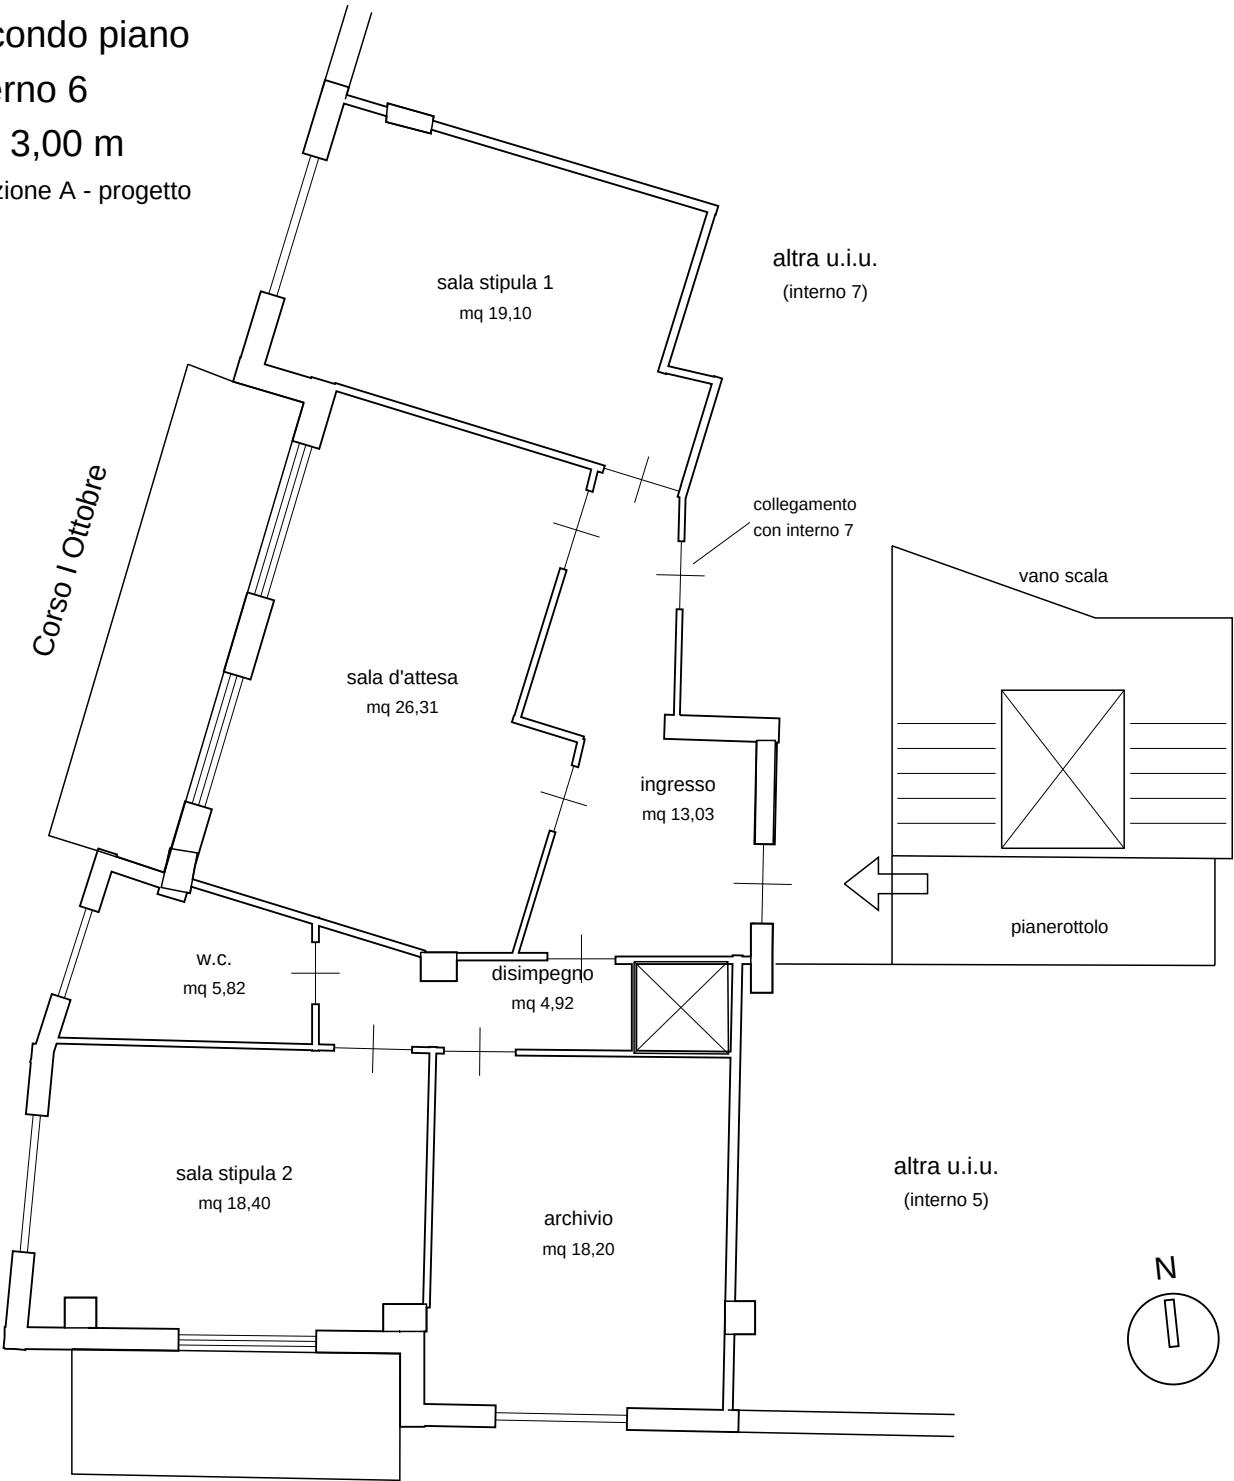


Via San Francesco D'Assisi

Interno 6 - secondo piano - adeguamento a studio notarile

Via San Francesco D'Assisi n. 6 - Maddaloni (CE) - Catasto Fabbricati: foglio 9, particella 663, subalterno 12

Sovrapposto: demolizioni e nuove opere

Tavola 2 di 3 - Scala 1:100

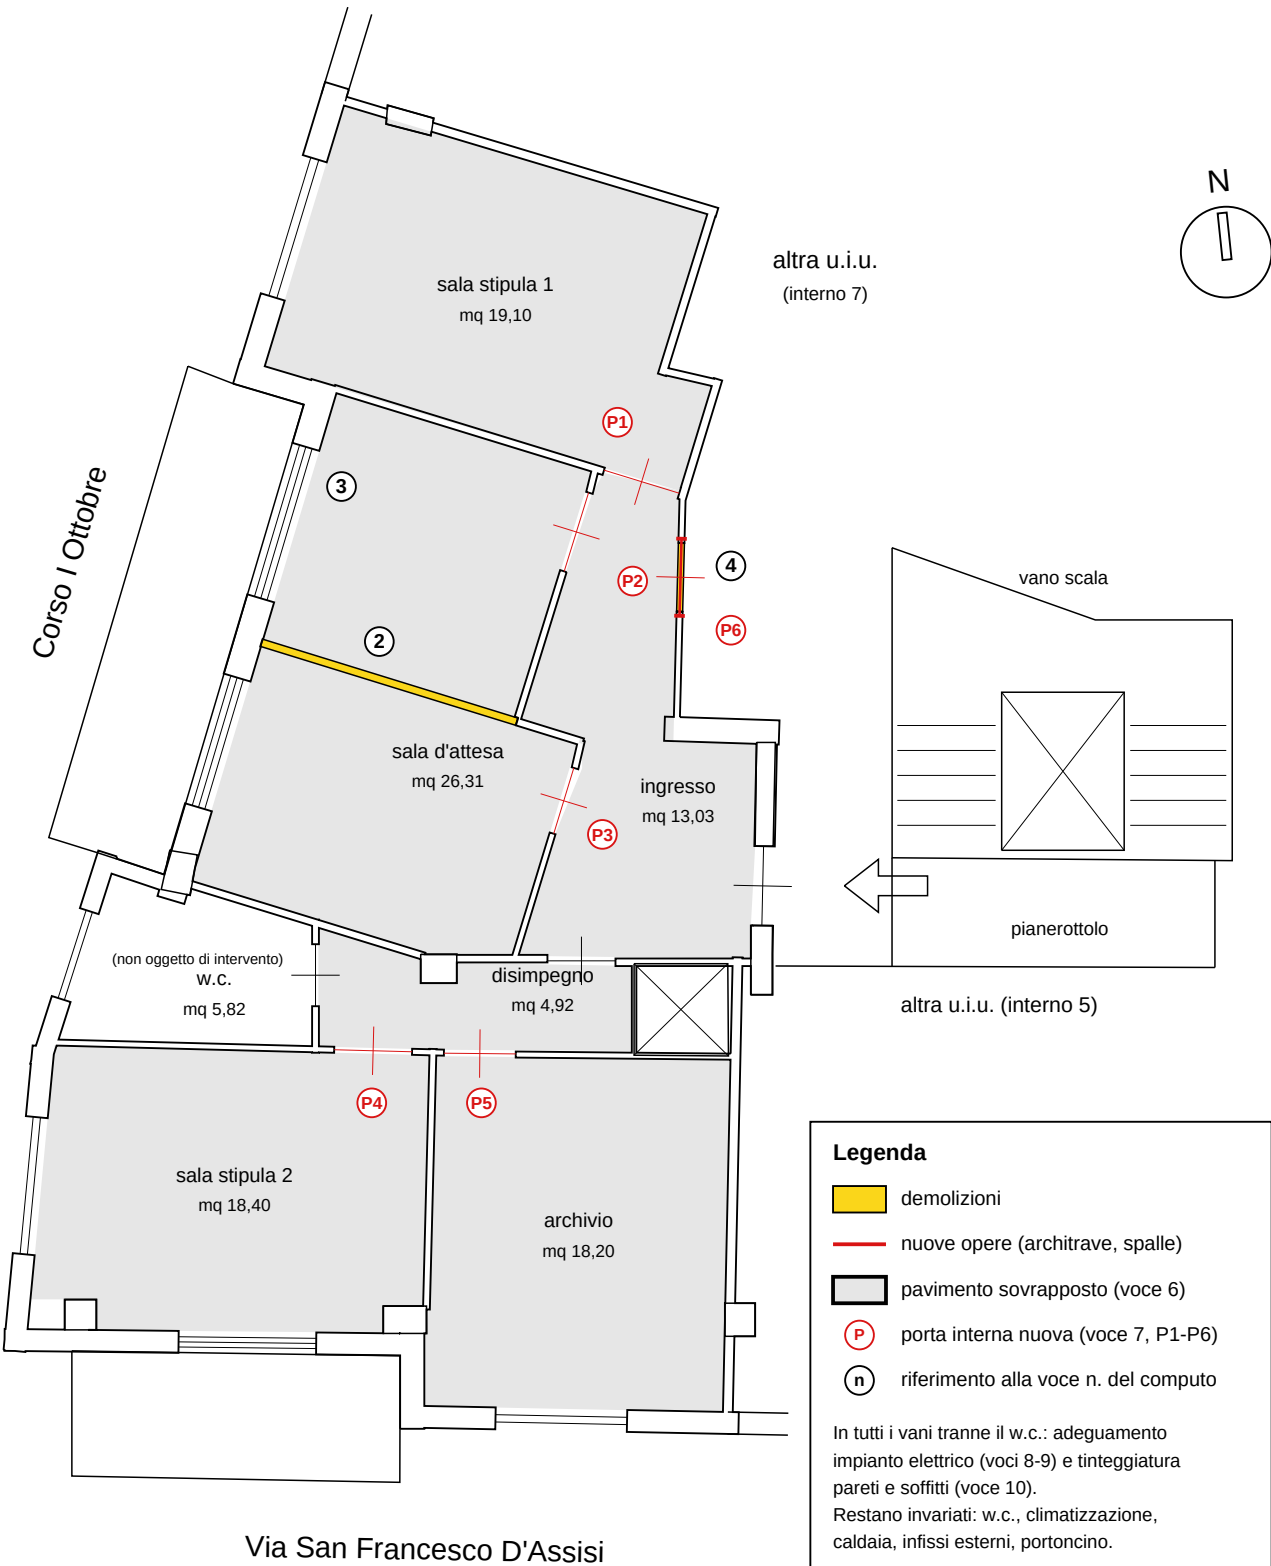

Interno 6 - secondo piano - adeguamento a studio notarile

Via San Francesco D'Assisi n. 6 - Maddaloni (CE) - Catasto Fabbricati: foglio 9, particella 663, subalterno 12

Quadro economico di massima - finiture di tipo medio Tavola 3 di 3 - Importi in euro, IVA esclusa

N.	Lavorazione	U.M.	Quantità	Prezzo unit. (€)	Importo (€)
A	Oneri di cantiere				
1	Allestimento, protezioni, pulizie finali, trasporto e smaltimento dei materiali di risulta	a corpo	1	900,00	900,00
B	Demolizioni e rimozioni				
2	Demolizione del tramezzo tra ex cucina ed ex camera (sp. 10 cm, h 3,00 m)	m²	10,59	25,00	264,75
3	Smontaggio della cucina e chiusura degli attacchi idrici e dello scarico	a corpo	1	450,00	450,00
C	Murature e intonaci				
4	Apertura del vano di collegamento con l'interno 7 (luce 0,90 x 2,10 m), con architrave in acciaio, spallette e riprese su entrambi i lati	a corpo	1	2.200,00	2.200,00
5	Riprese di intonaco agli attacchi del tramezzo demolito (pareti e soffitto)	a corpo	1	650,00	650,00
D	Pavimenti				
6	Pavimento sovrapposto in SPC/LVT su pavimento esistente, con materassino, battiscopa e profili	m²	99,96	42,00	4.198,32
E	Porte interne				
7	Porta interna tamburata laccata, con telaio e coprifili, maniglia, posa su vano esistente o nuovo	n.	6	480,00	2.880,00
F	Impianto elettrico				
8	Adeguamento dell'impianto elettrico per uso ufficio: quadro, linee, punti luce e presa, prese dati, dichiarazione di conformità	m²	99,96	50,00	4.998,00
9	Corpi illuminanti a LED a plafone, compresa posa	n.	12	110,00	1.320,00
G	Pitture				
10	Stuccatura localizzata e tinteggiatura con idropittura lavabile, due mani, pareti e soffitti	m²	379,43	8,50	3.225,16
	Totale lavori				21.086,23
	Imprevisti (5% dei lavori)				1.054,31
	Spese tecniche: pratica edilizia, verifica strutturale del vano di collegamento, variazione catastale, direzione lavori	a corpo	1	3.500,00	3.500,00
	Totale complessivo (IVA esclusa)				25.640,54

Opere escluse

w.c. esistente, impianto di climatizzazione e caldaia, infissi esterni, portoncino d'ingresso, arredi.

Superfici di riferimento

superficie netta oggetto di intervento (escluso il w.c.) mq 99,96; pareti e soffitti da tinteggiare mq 379,43; altezza dei vani m 3,00.